


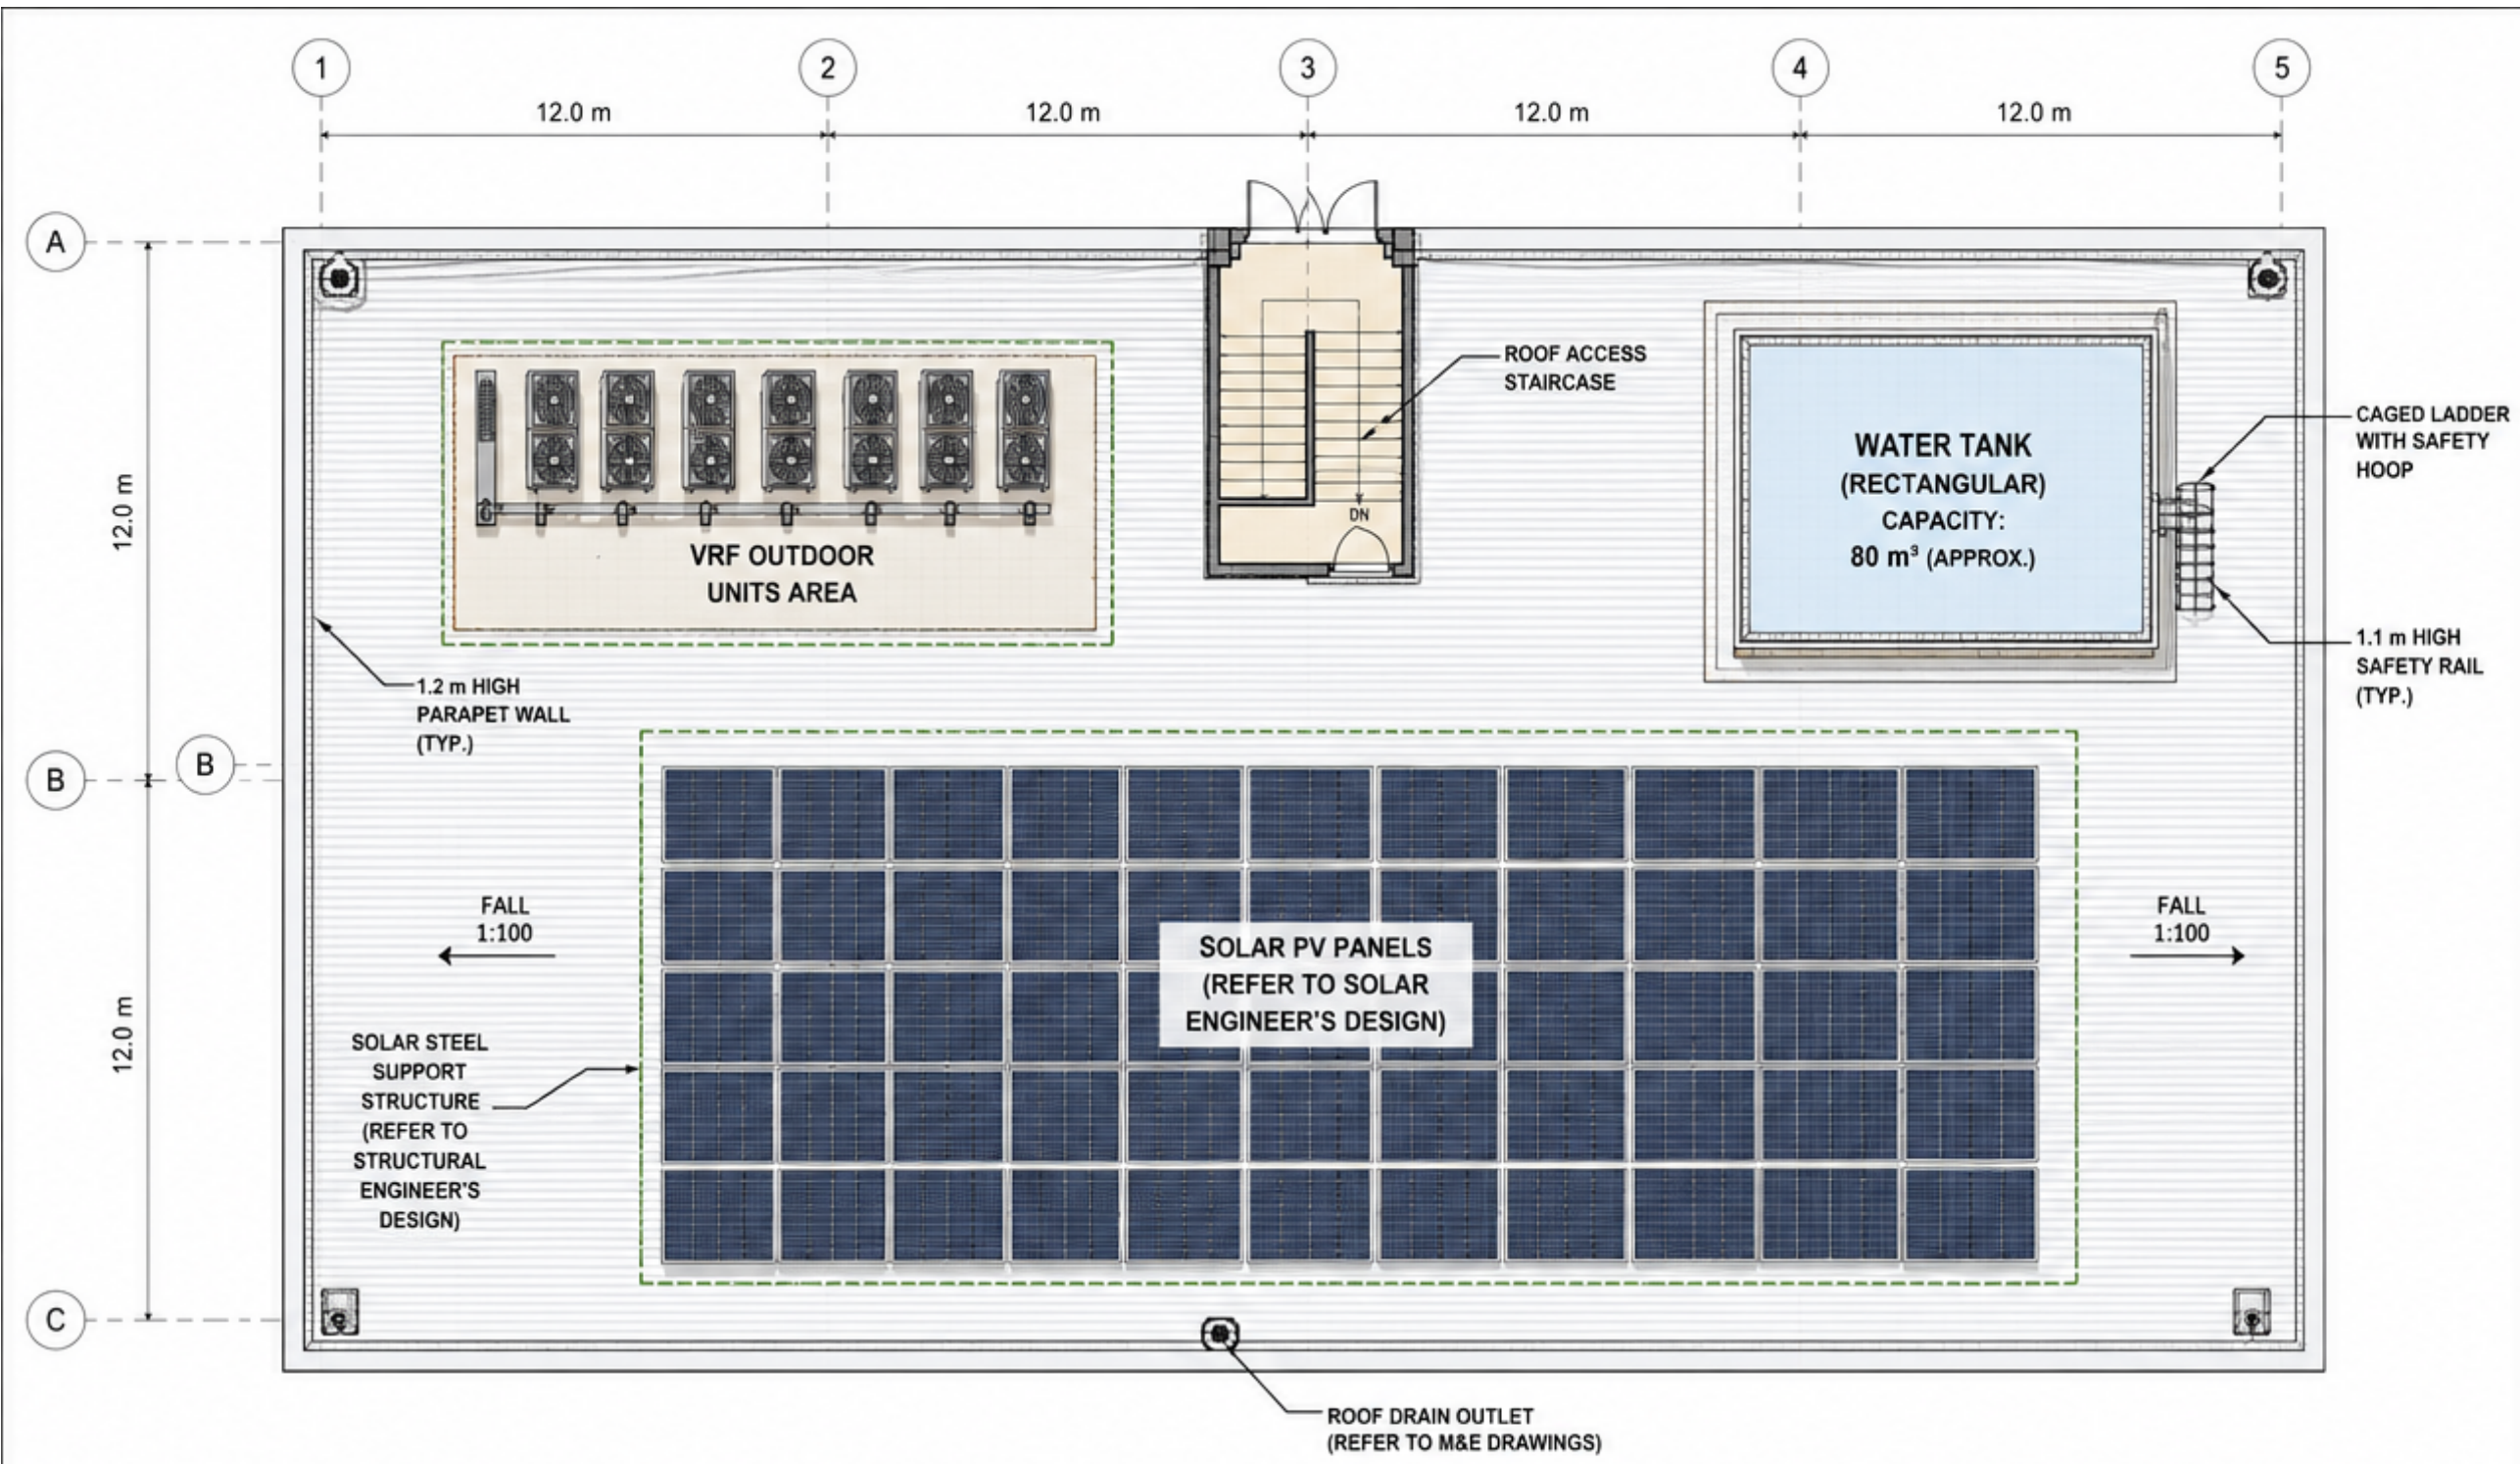

FW-003

FACILITY WORKS MONITOR

ROOF PLAN

LEGEND

- ROOF ACCESS / STAIRCASE
- WATER TANK
- ROOF AREA
- VRF OUTDOOR UNITS AREA
- SOLAR STEEL STRUCTURE AREA
- SINGLE SWING DOOR
- ROOF DRAIN / SCUPPER
- CAGED LADDER
- FALL DIRECTION (1:100)


ROOF PLAN SUMMARY	
ROOF ACCESS STAIRCASE	12.0 m²
VRF OUTDOOR UNITS AREA	42.0 m²
WATER TANK & PLATFORM	56.0 m²
SOLAR PV PANELS AREA	450.0 m² (APPROX.)
ROOF AREA (TOTAL)	820.0 m² (APPROX.)

PROJECT
FACILITY WORKS MONITOR

DRAWING TITLE
ROOF PLAN

DRAWING NO. FW-003	REV. A
------------------------------	------------------

DATE 25 MAY 2024	SCALE 1 : 150 (A3)
---------------------	-----------------------

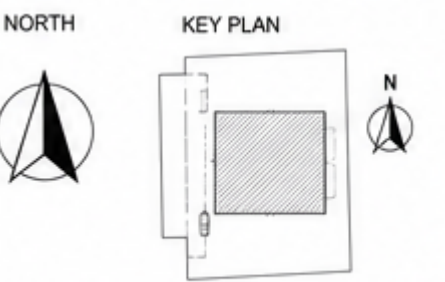

- NOTES:**
- All roof penetrations, flashings and waterproofing to be in accordance with manufacturer's recommendations.
 - All roof drains to be connected to internal downpipes. Refer to M&E drawings.
 - Fall to roof drains at minimum 1:100.
 - All railings and access system to comply with SS 550 and relevant authorities' requirements.

- ROOF ACCESS**
- Lockable roof access door from 2nd Storey staircase.
 - Access provided for maintenance of VRF units, water tank and solar PV system.
 - Provide safe access walkway around equipment and tank.

- MECHANICAL**
- VRF outdoor units in dedicated area with maintenance clearance.
 - Refer to M&E drawings for quantity, loading and mounting details.

- SOLAR PV SYSTEM (INDICATIVE)**
- Solar PV system design by specialist.
 - Solar steel support structure to be designed to structural engineer's design.
 - Provide maintenance access walkway as required.