

FW-004

FACILITY WORKS MONITOR ELEVATIONS

LEGEND - FINISHES

	M1	METAL CLADDING (ROOF & PARAPET)
	M2	ALUMINIUM LOUVRE (SUNSHADE)
	P1	PAINT FINISH - LIGHT GREY
	P2	PAINT FINISH - MEDIUM GREY
	G1	TINTED GLASS
	MF	METAL CANOPY
	CR	CONCRETE RENDER - UTILITY BUILDING
	RA	ROOF ACCESS LADDER (WITH SAFETY HOOP)

GENERAL NOTES

- ALL LEVELS ARE IN METRES.
- ALL DIMENSIONS ARE TO FINISHED FACES UNLESS NOTED OTHERWISE.
- EXTERNAL DOORS AND WINDOWS TO BE ALUMINIUM FRAME.
- ALL LOUVRES TO ENGINEER'S SPECIFICATION.
- REFER TO FLOOR PLANS FOR OPENING LOCATIONS.

PROJECT
FACILITY WORKS MONITOR


DRAWING TITLE
ELEVATIONS

DRAWING NO.
FW-004


REV.
A

DATE
25 MAY 2024


SCALE
1 : 150 (A3)

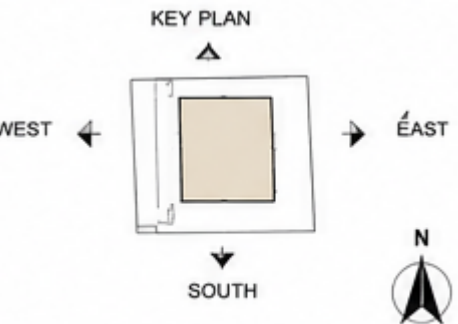


NORTH ELEVATION (FRONT)

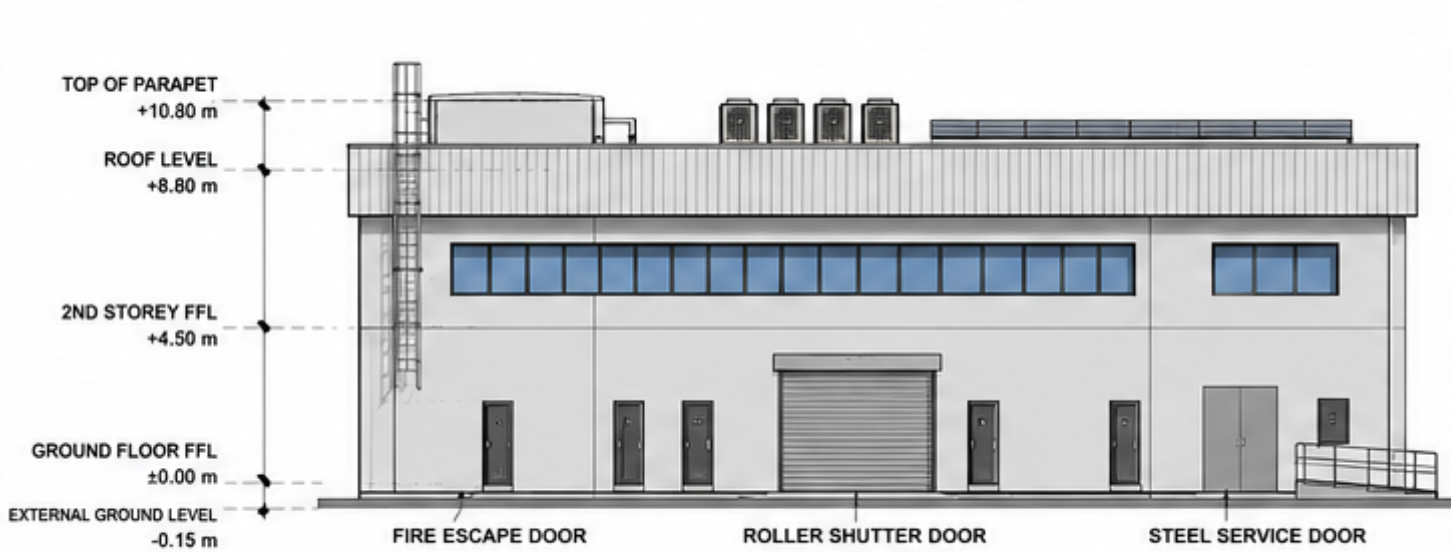

SOUTH ELEVATION (REAR)

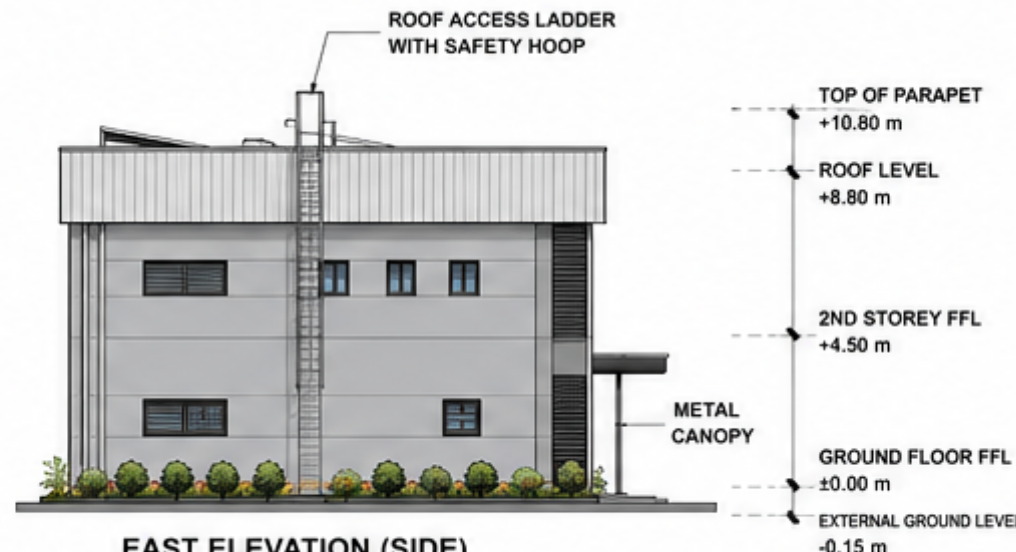

EAST ELEVATION (SIDE)

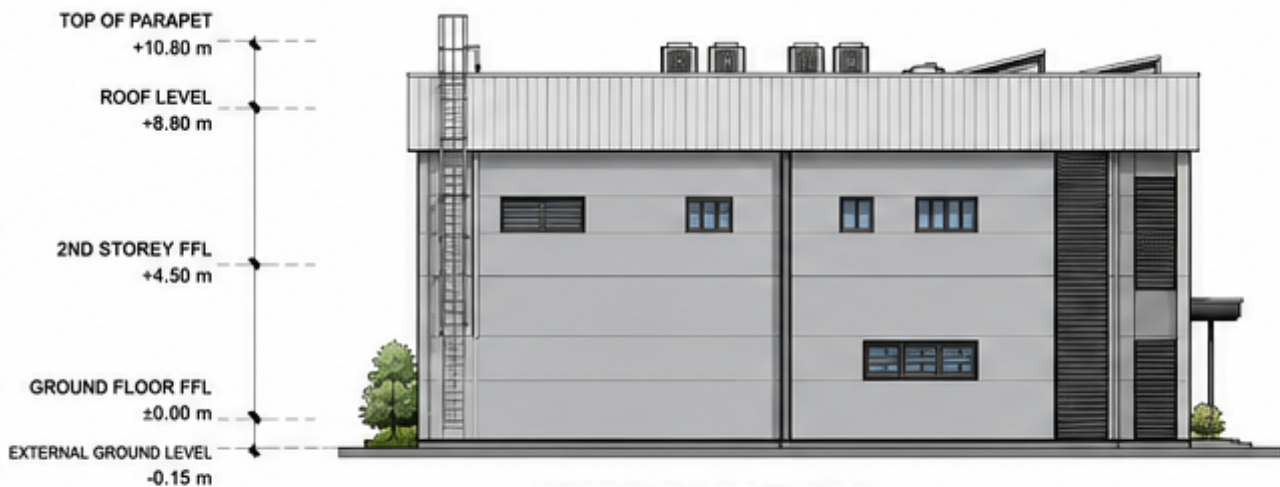

WEST ELEVATION (SIDE)

EXTERNAL FINISHES SCHEDULE

M1	METAL CLADDING (ROOF & PARAPET)	COLORBOND / EQUIVALENT
M2	ALUMINIUM LOUVRE (SUNSHADE)	POWDER COATED
P1	PAINT FINISH - LIGHT GREY	EXTERIOR GRADE PAINT
P2	PAINT FINISH - MEDIUM GREY	EXTERIOR GRADE PAINT
G1	TINTED GLASS	PERFORMANCE GLASS
MF	METAL CANOPY	POWDER COATED STEEL
CR	CONCRETE RENDER (UTILITY BLDG)	WEATHER RESISTANT FINISH

BUILDING HEIGHT

TOP OF PARAPET	+10.80 m
ROOF LEVEL	+8.80 m
2ND STOREY FFL	+4.50 m
GROUND FLOOR FFL	±0.00 m

MAX BUILDING HEIGHT
(From External Ground Level) 10.95 m